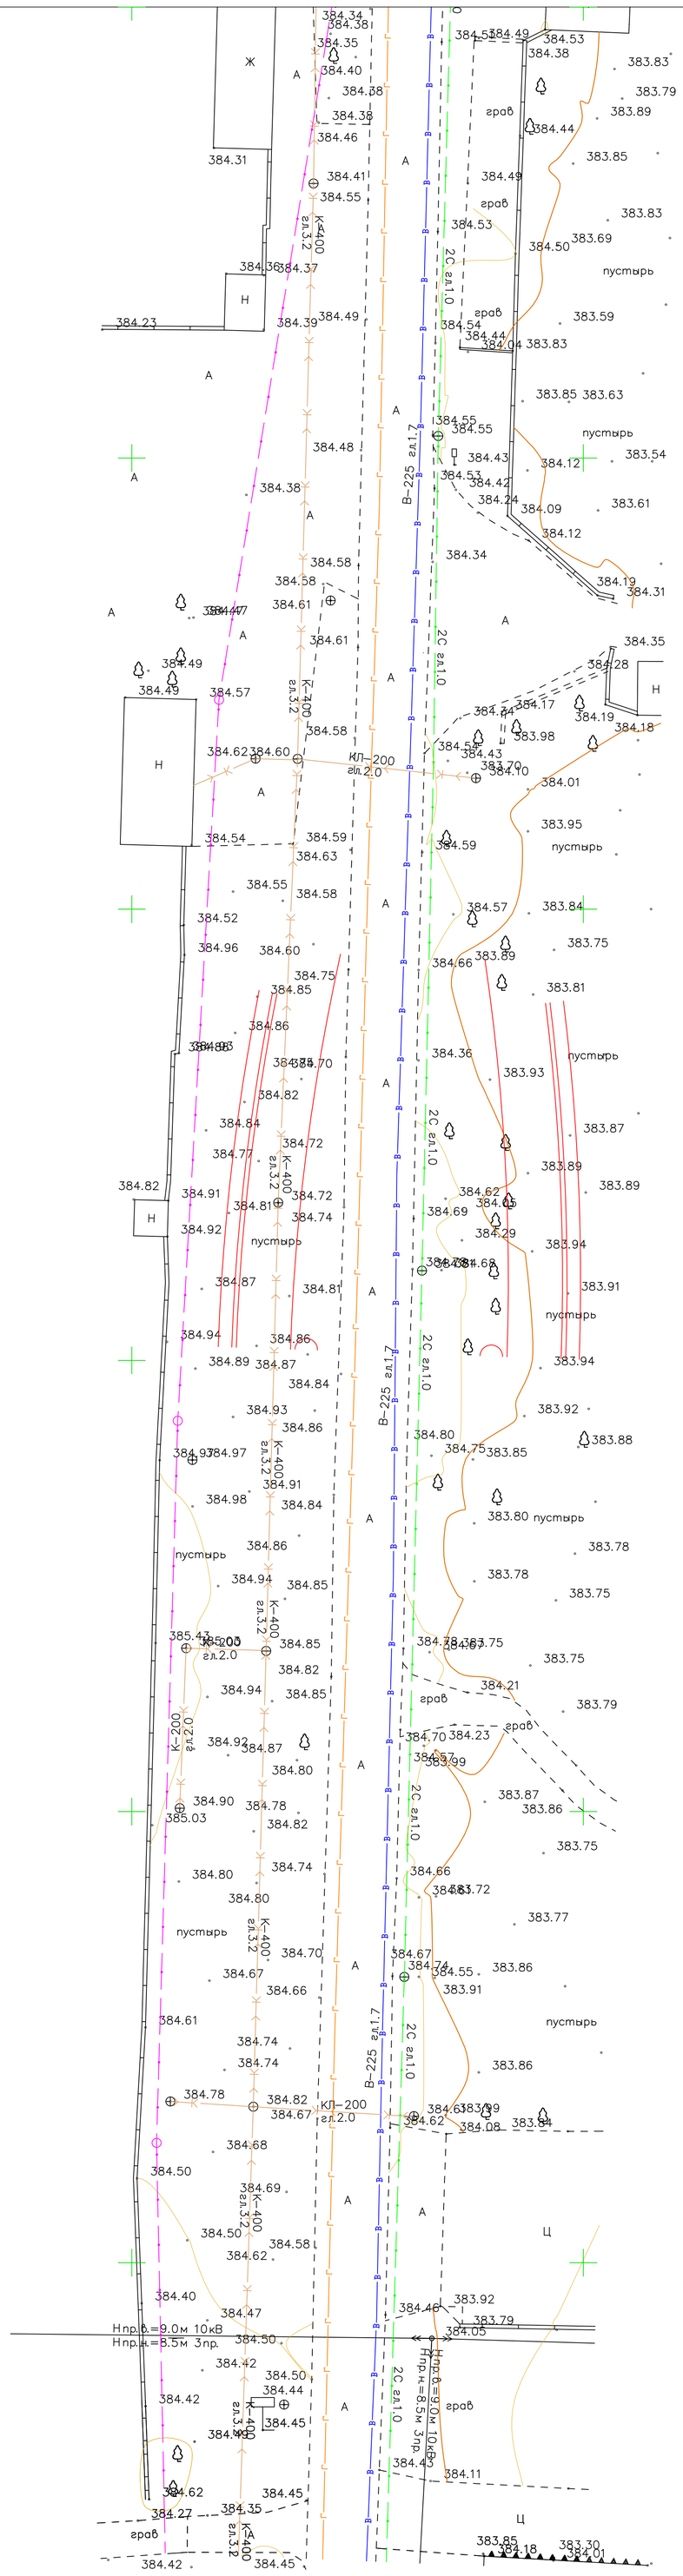

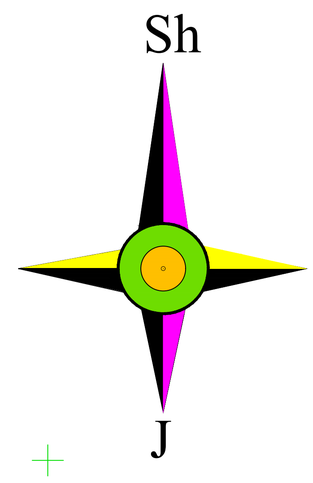

				M.O'.		Inventar №
Lavozim		F.I.SH.	Imzo	Sana	Obyekt: O'zbekiston kochasini Topografik tasvirini yaratish	Shartnoma №
Direktori		Fayziyev Sh.				
Direktori o'rinbosari		Ashurov S.				
Partiya boshlig'i		Jo'rayev I.				
Topog.	yer usti	Ashurov S.			Bosqich / Varaq / Varaqlar soni	
	yer osti				Topografik tasvir	1 / 1
Tahrirlovchi		Jo'rayev I.			Masshtab 1:500	© Topografiya va Raqamli Kadastr MCHJ
Operator		Bekmurodov D.			WGS 84 koordinatalar tizimi	
					Boltiqbo'yi balandliklar tizimi	
					Relyef kesimi oralig'i 0.5 m	Qarshi sh. "08" Iyun 2025y.